



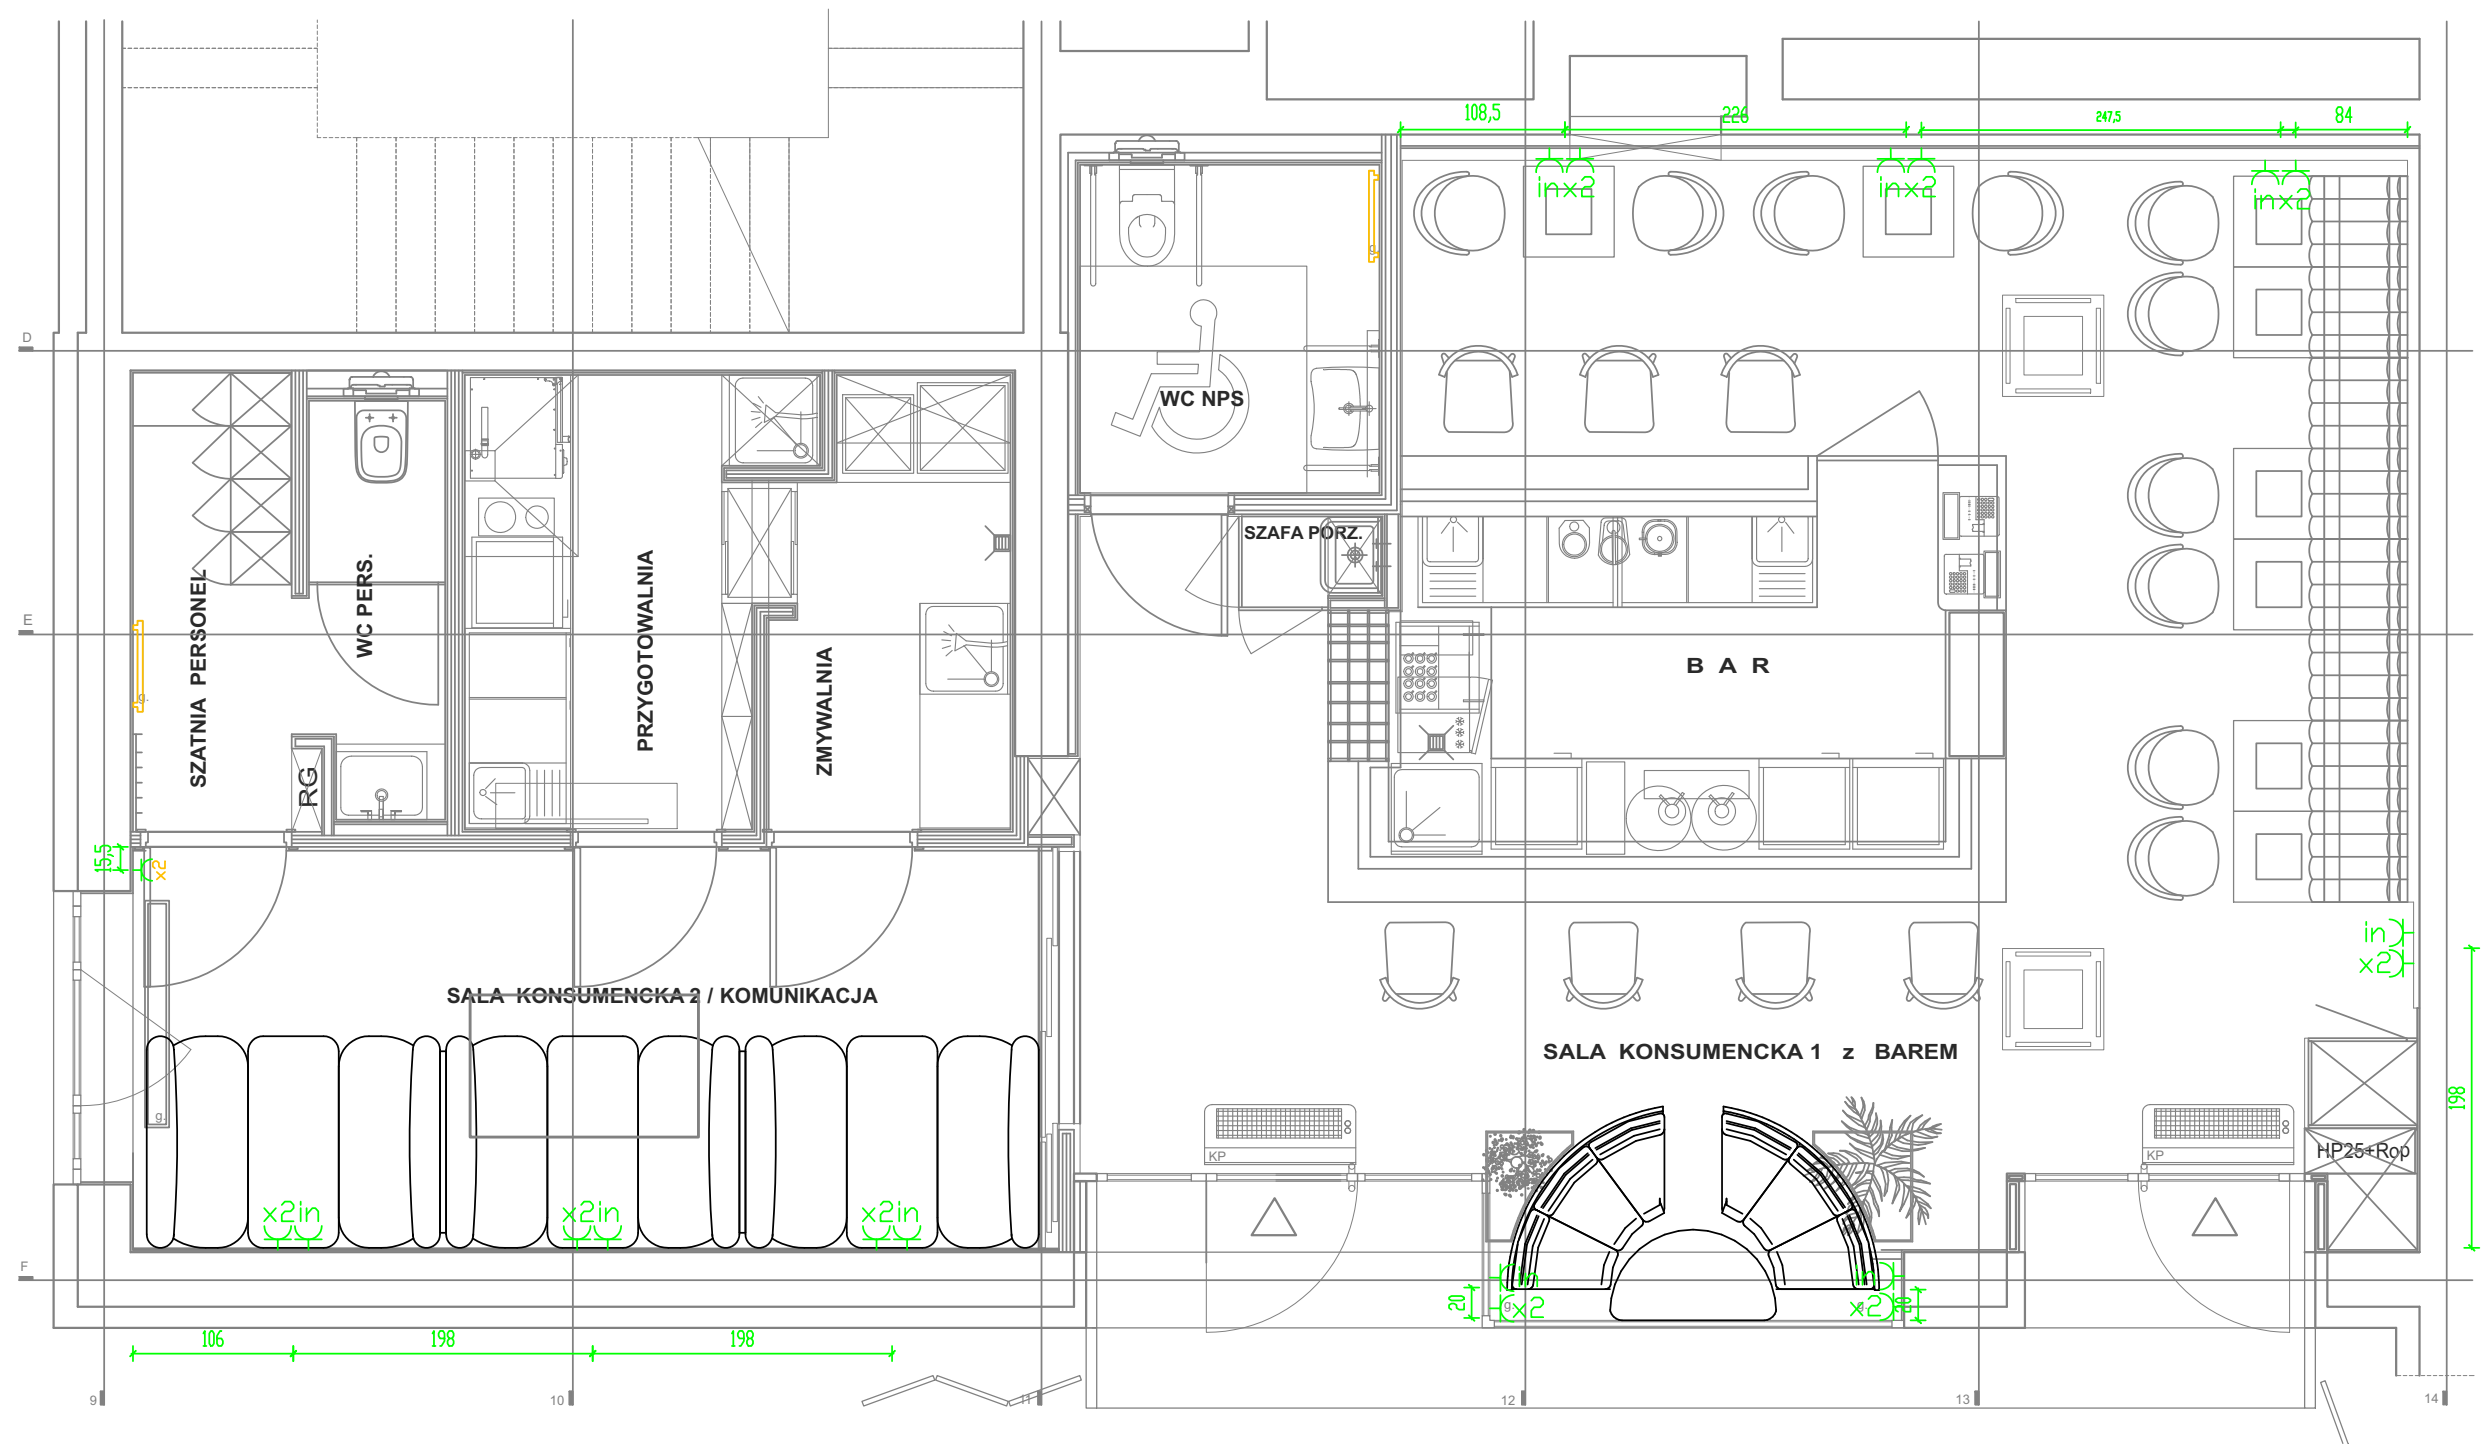


Część elektryczna dla klientów - nowy projekt

gniazda na wysokości 20cm od docelowej podłogi

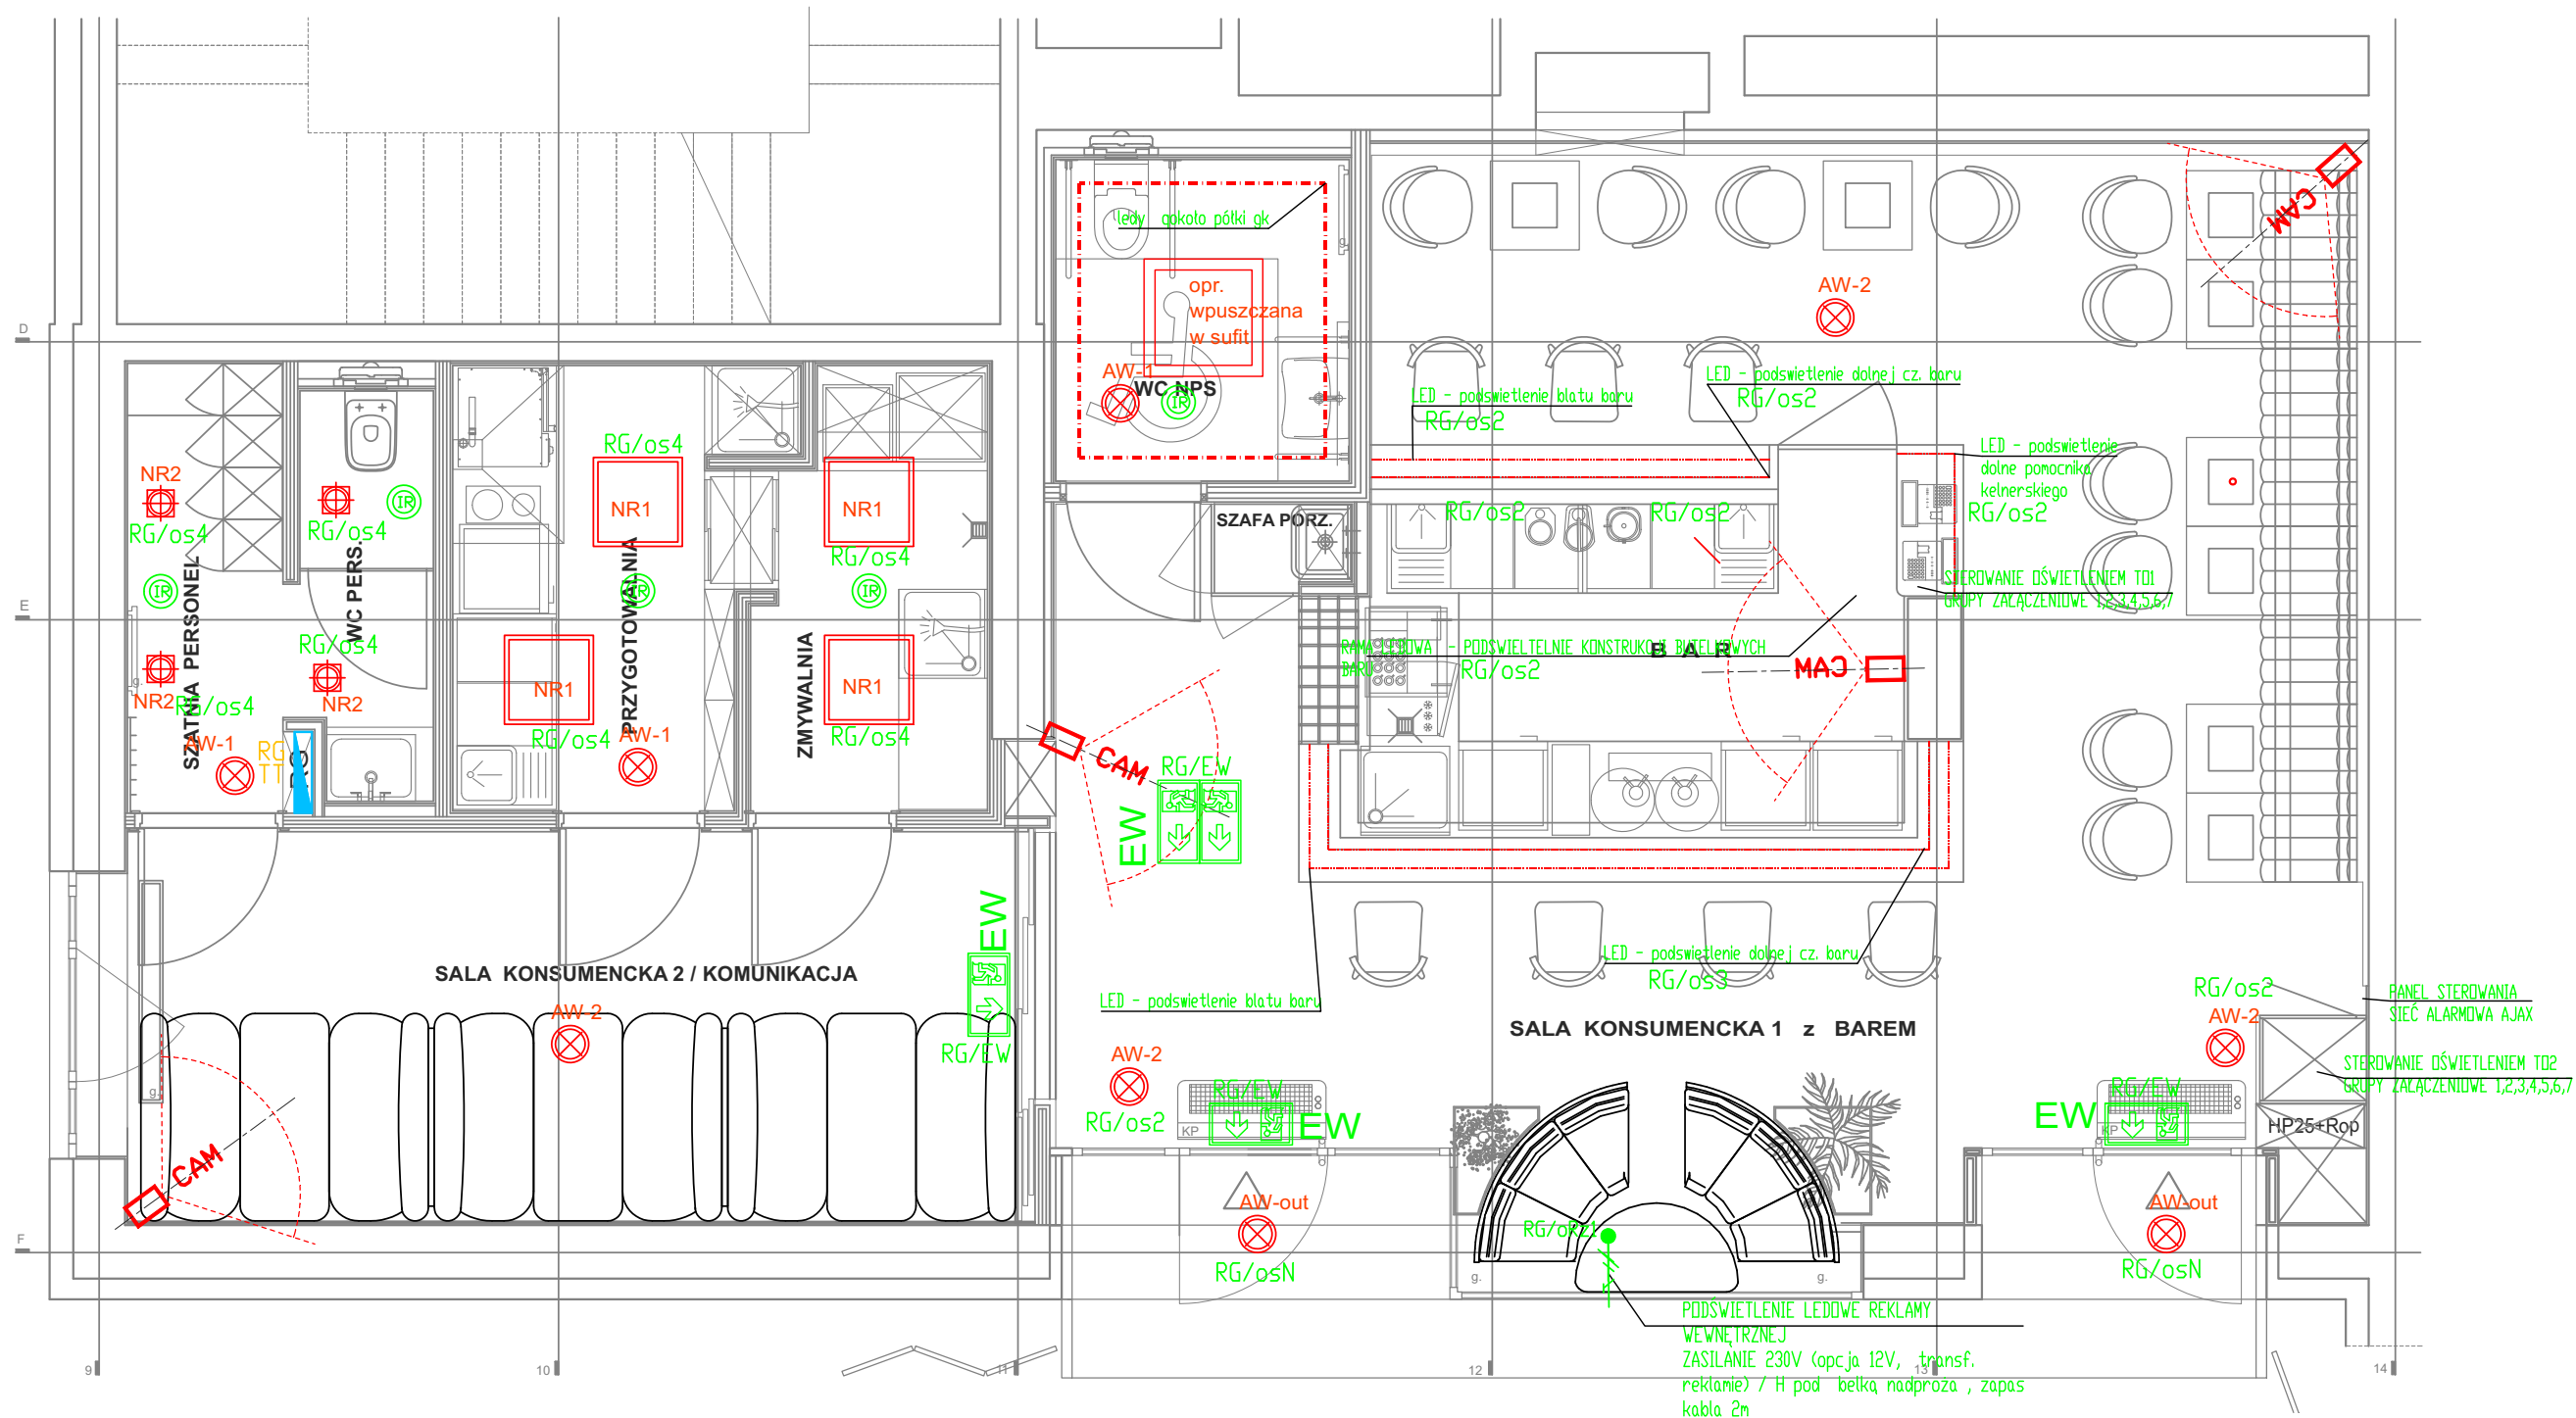

Część oświetlenia technicznego - pozostawiona z poprzedniego projektu

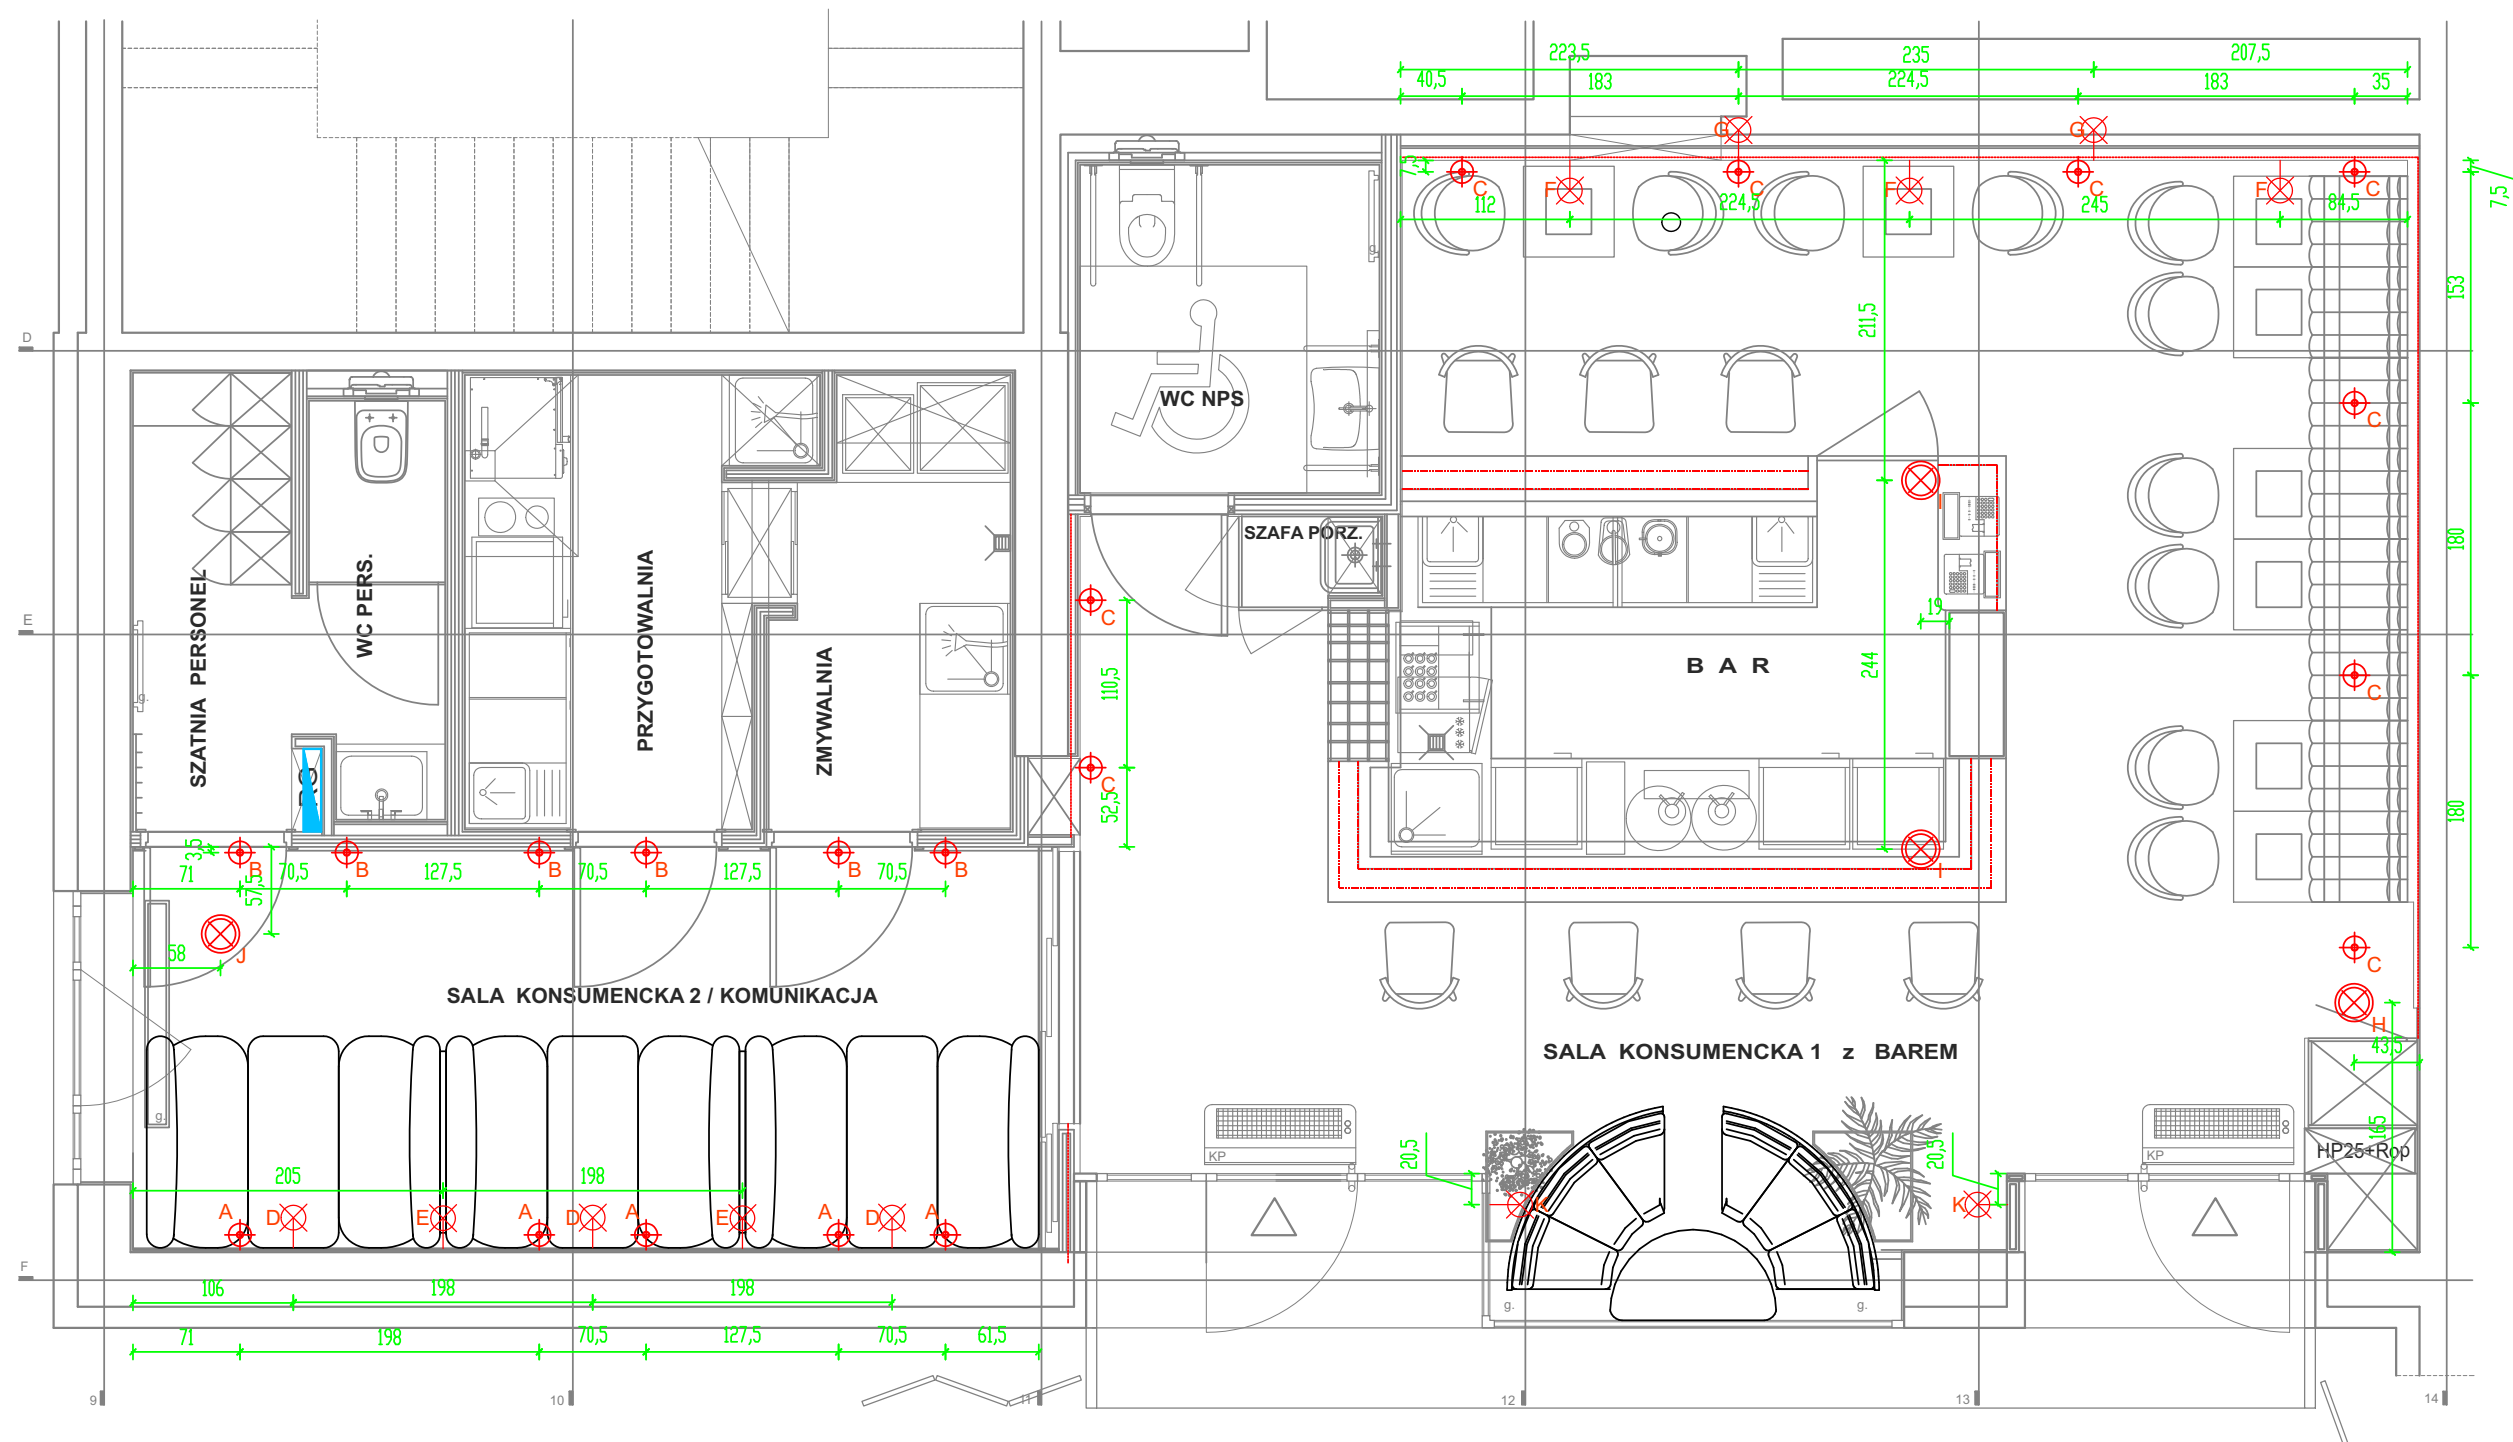


Część oświetlenia dekoracyjnego - nowy projekt

Litery przy symbolach oznaczają grupę oświetlenia
Całe oświetlenie z możliwością ściemniania
wypust kinkietu na wysokości 15cm od podłogi
wypust pod LED w barze na wysokości 105cm

LED w ścianie - poprowadzony w bruździe 5x15cm (głębokośćxwysokość) na wysokości 150cm

- ⊗ wypust pod lampy dekoracyjne - sufitowe połączone szerego, natynkowo
- ⊙ spot natynkowy
- ⊗⊙ kinkiet (15cm od podłogi)

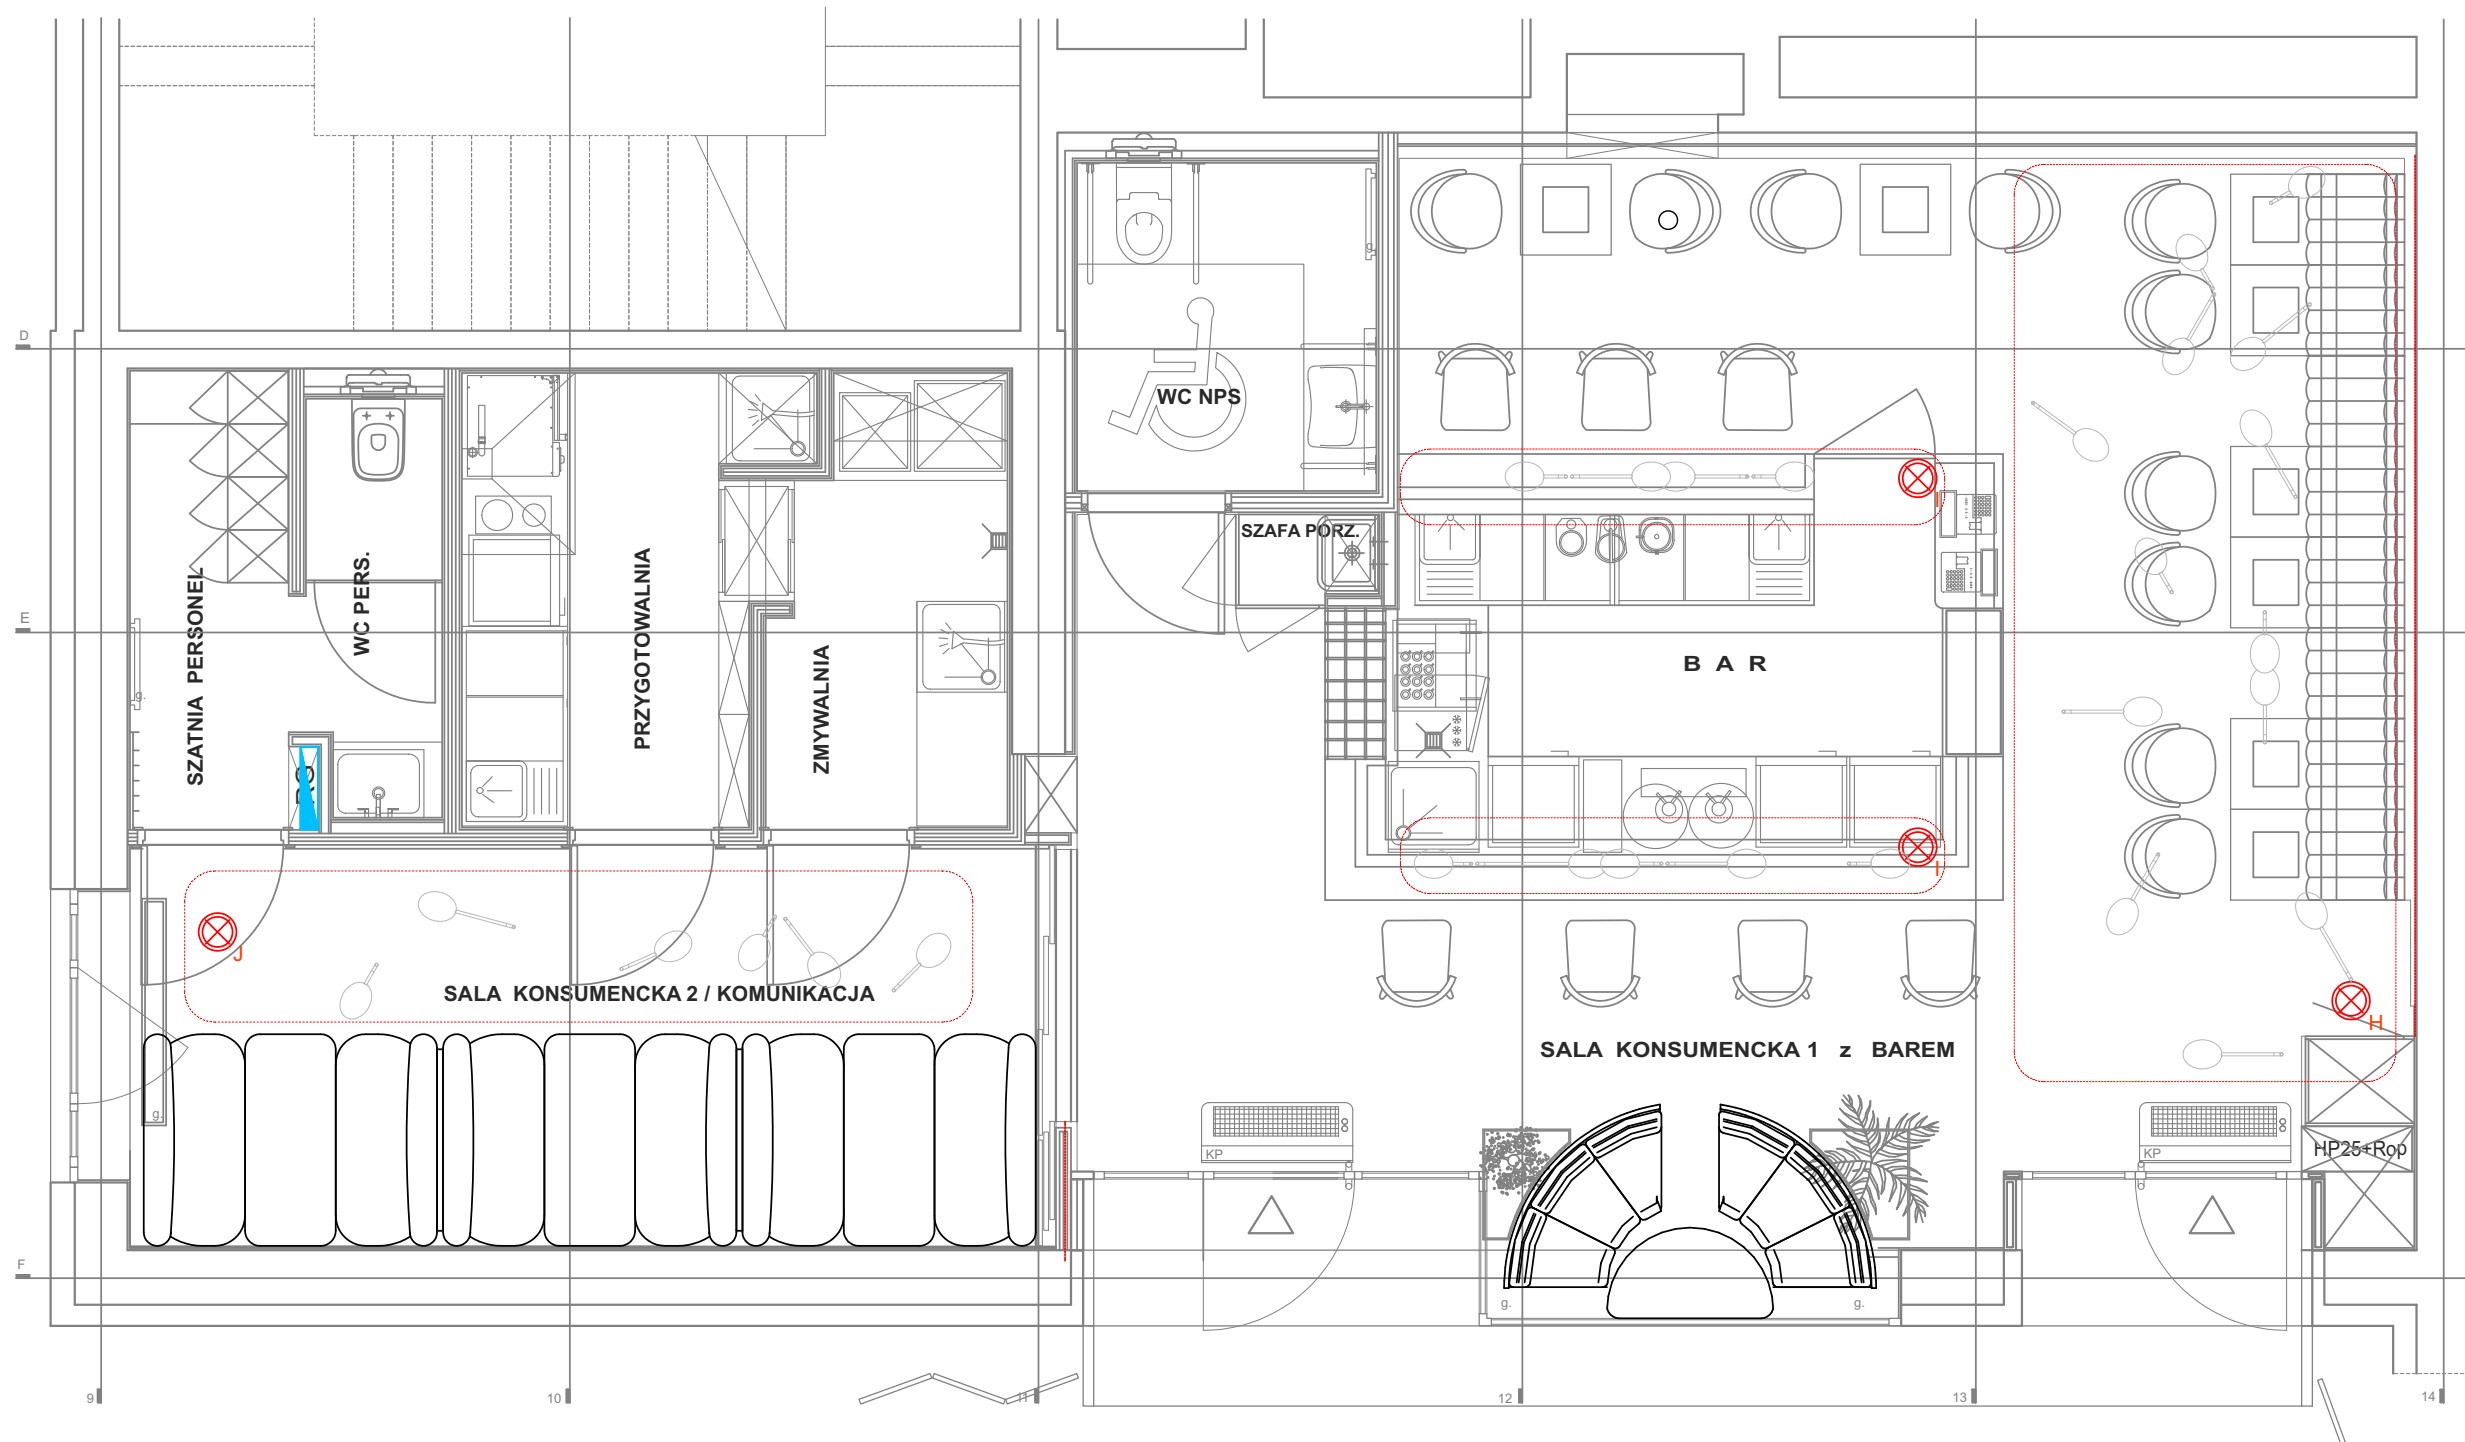

sugerowane rozmieszczenie opraw dekoracyjnych i ich grupy