


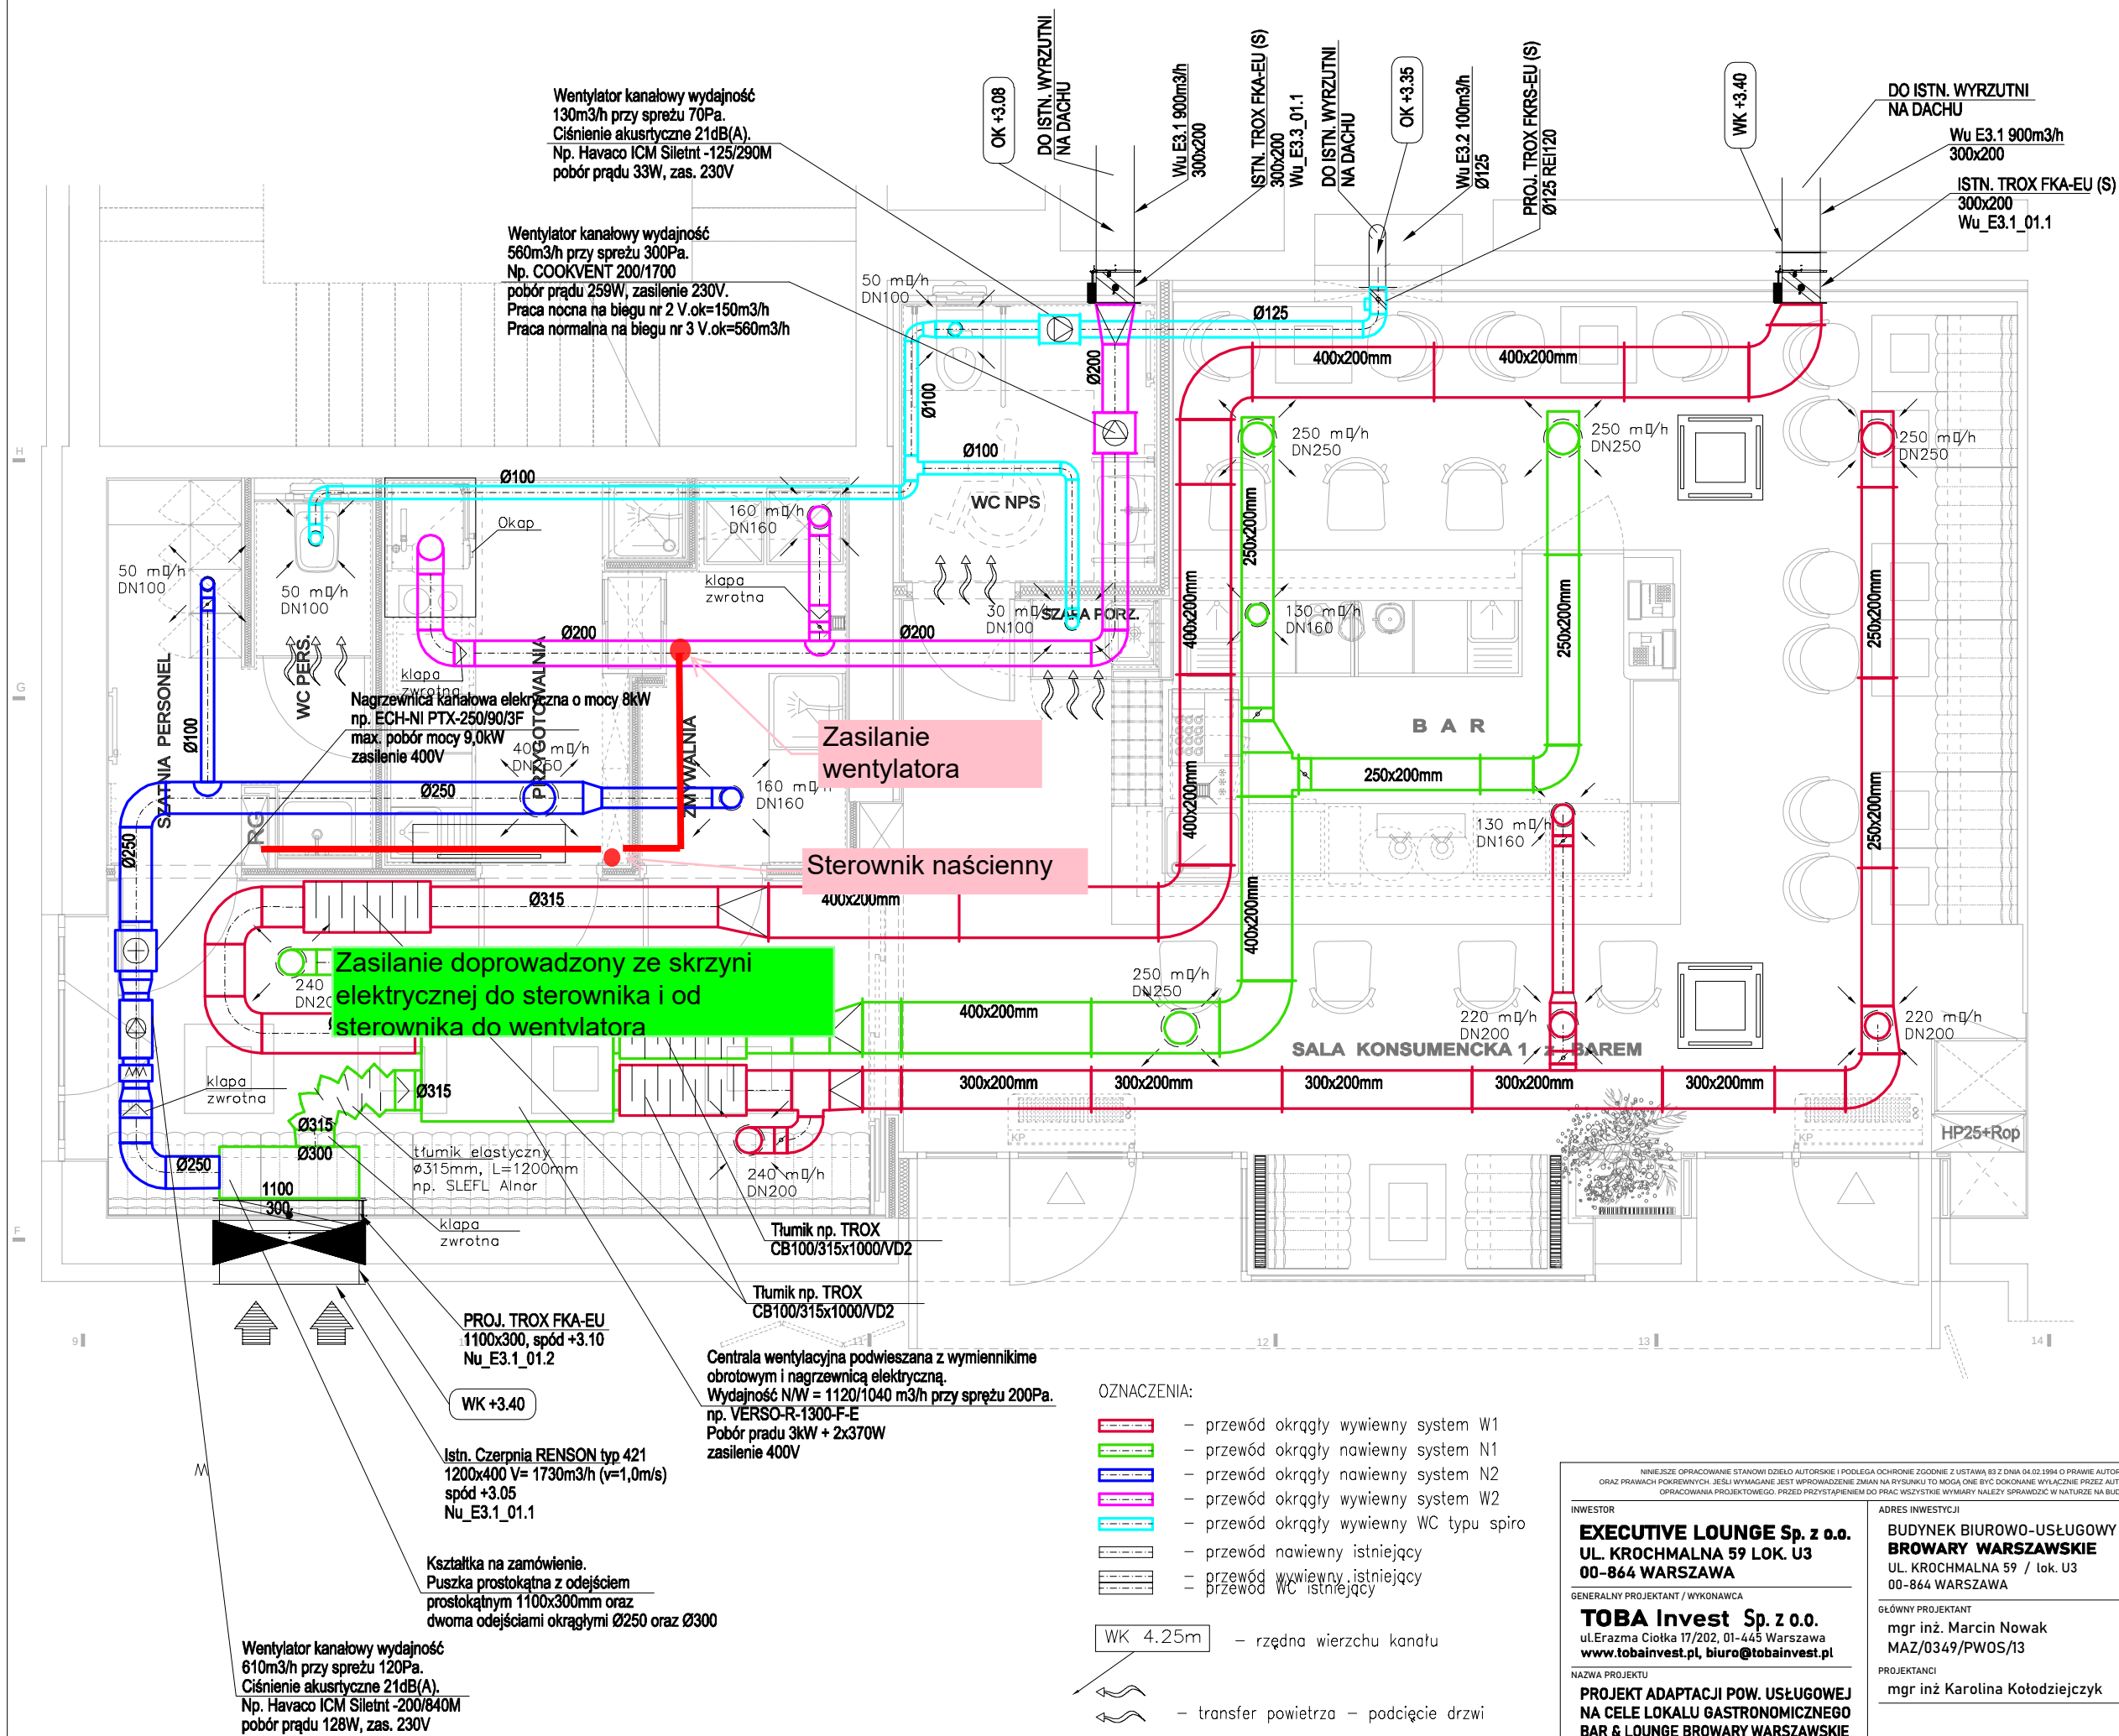

- OZNACZENIA:
- przewód okrągły wywiewny system W1
 - przewód okrągły nawiewny system N1
 - przewód okrągły nawiewny system N2
 - przewód okrągły wywiewny system W2
 - przewód okrągły wywiewny WC typu spiro
 - przewód nawiewny istniejący
 - przewód wywiewny istniejący
 - przewód WC istniejący

WK 4.25m – rzędna wierzchu kanału

transfer powietrza – podcięcie drzwi

INWESTOR

EXECUTIVE LOUNGE Sp. z o.o.
UL. KROCHMALNA 59 LOK. U3
00-864 WARSZAWA

GENERALNY PROJEKTANT / WYKONAWCA

TOBA Invest Sp. z o.o.
ul.Erasmia Ciołka 17/202, 01-445 Warszawa
www.tobainvest.pl, biuro@tobainvest.pl

NAZWA PROJEKTU

**PROJEKT ADAPTACJI POW. USŁUGOWEJ
NA CELE LOKALU GASTRONOMICZNEGO
BAR & LOUNGE BROWARY WARSZAWSKIE**

ADRES INWESTYCJI

**BUDYNEK BIUROWO-USŁUGOWY
BROWARY WARSZAWSKIE**
UL. KROCHMALNA 59 / lok. U3
00-864 WARSZAWA

GŁÓWNY PROJEKTANT

mgr inż. Marcin Nowak
MAZ/0349/PWOS/13

PROJEKTANCI

mgr inż. Karolina Kotodziejczyk

BRANŻA

SANITARNIA

PRZEZNACZENIE

PROJEKT WYKONAWCZY

TYTUŁ RYSUNKU

**INSTALACJA
WENTYLACJI I
KLIMATYZACJI**

DATA OPRACOWANIA


05.2021

SKALA / FORMAT

1:50 / A3

NR.RYS./REWIZJA

PW.S.01_rew.555_06.21

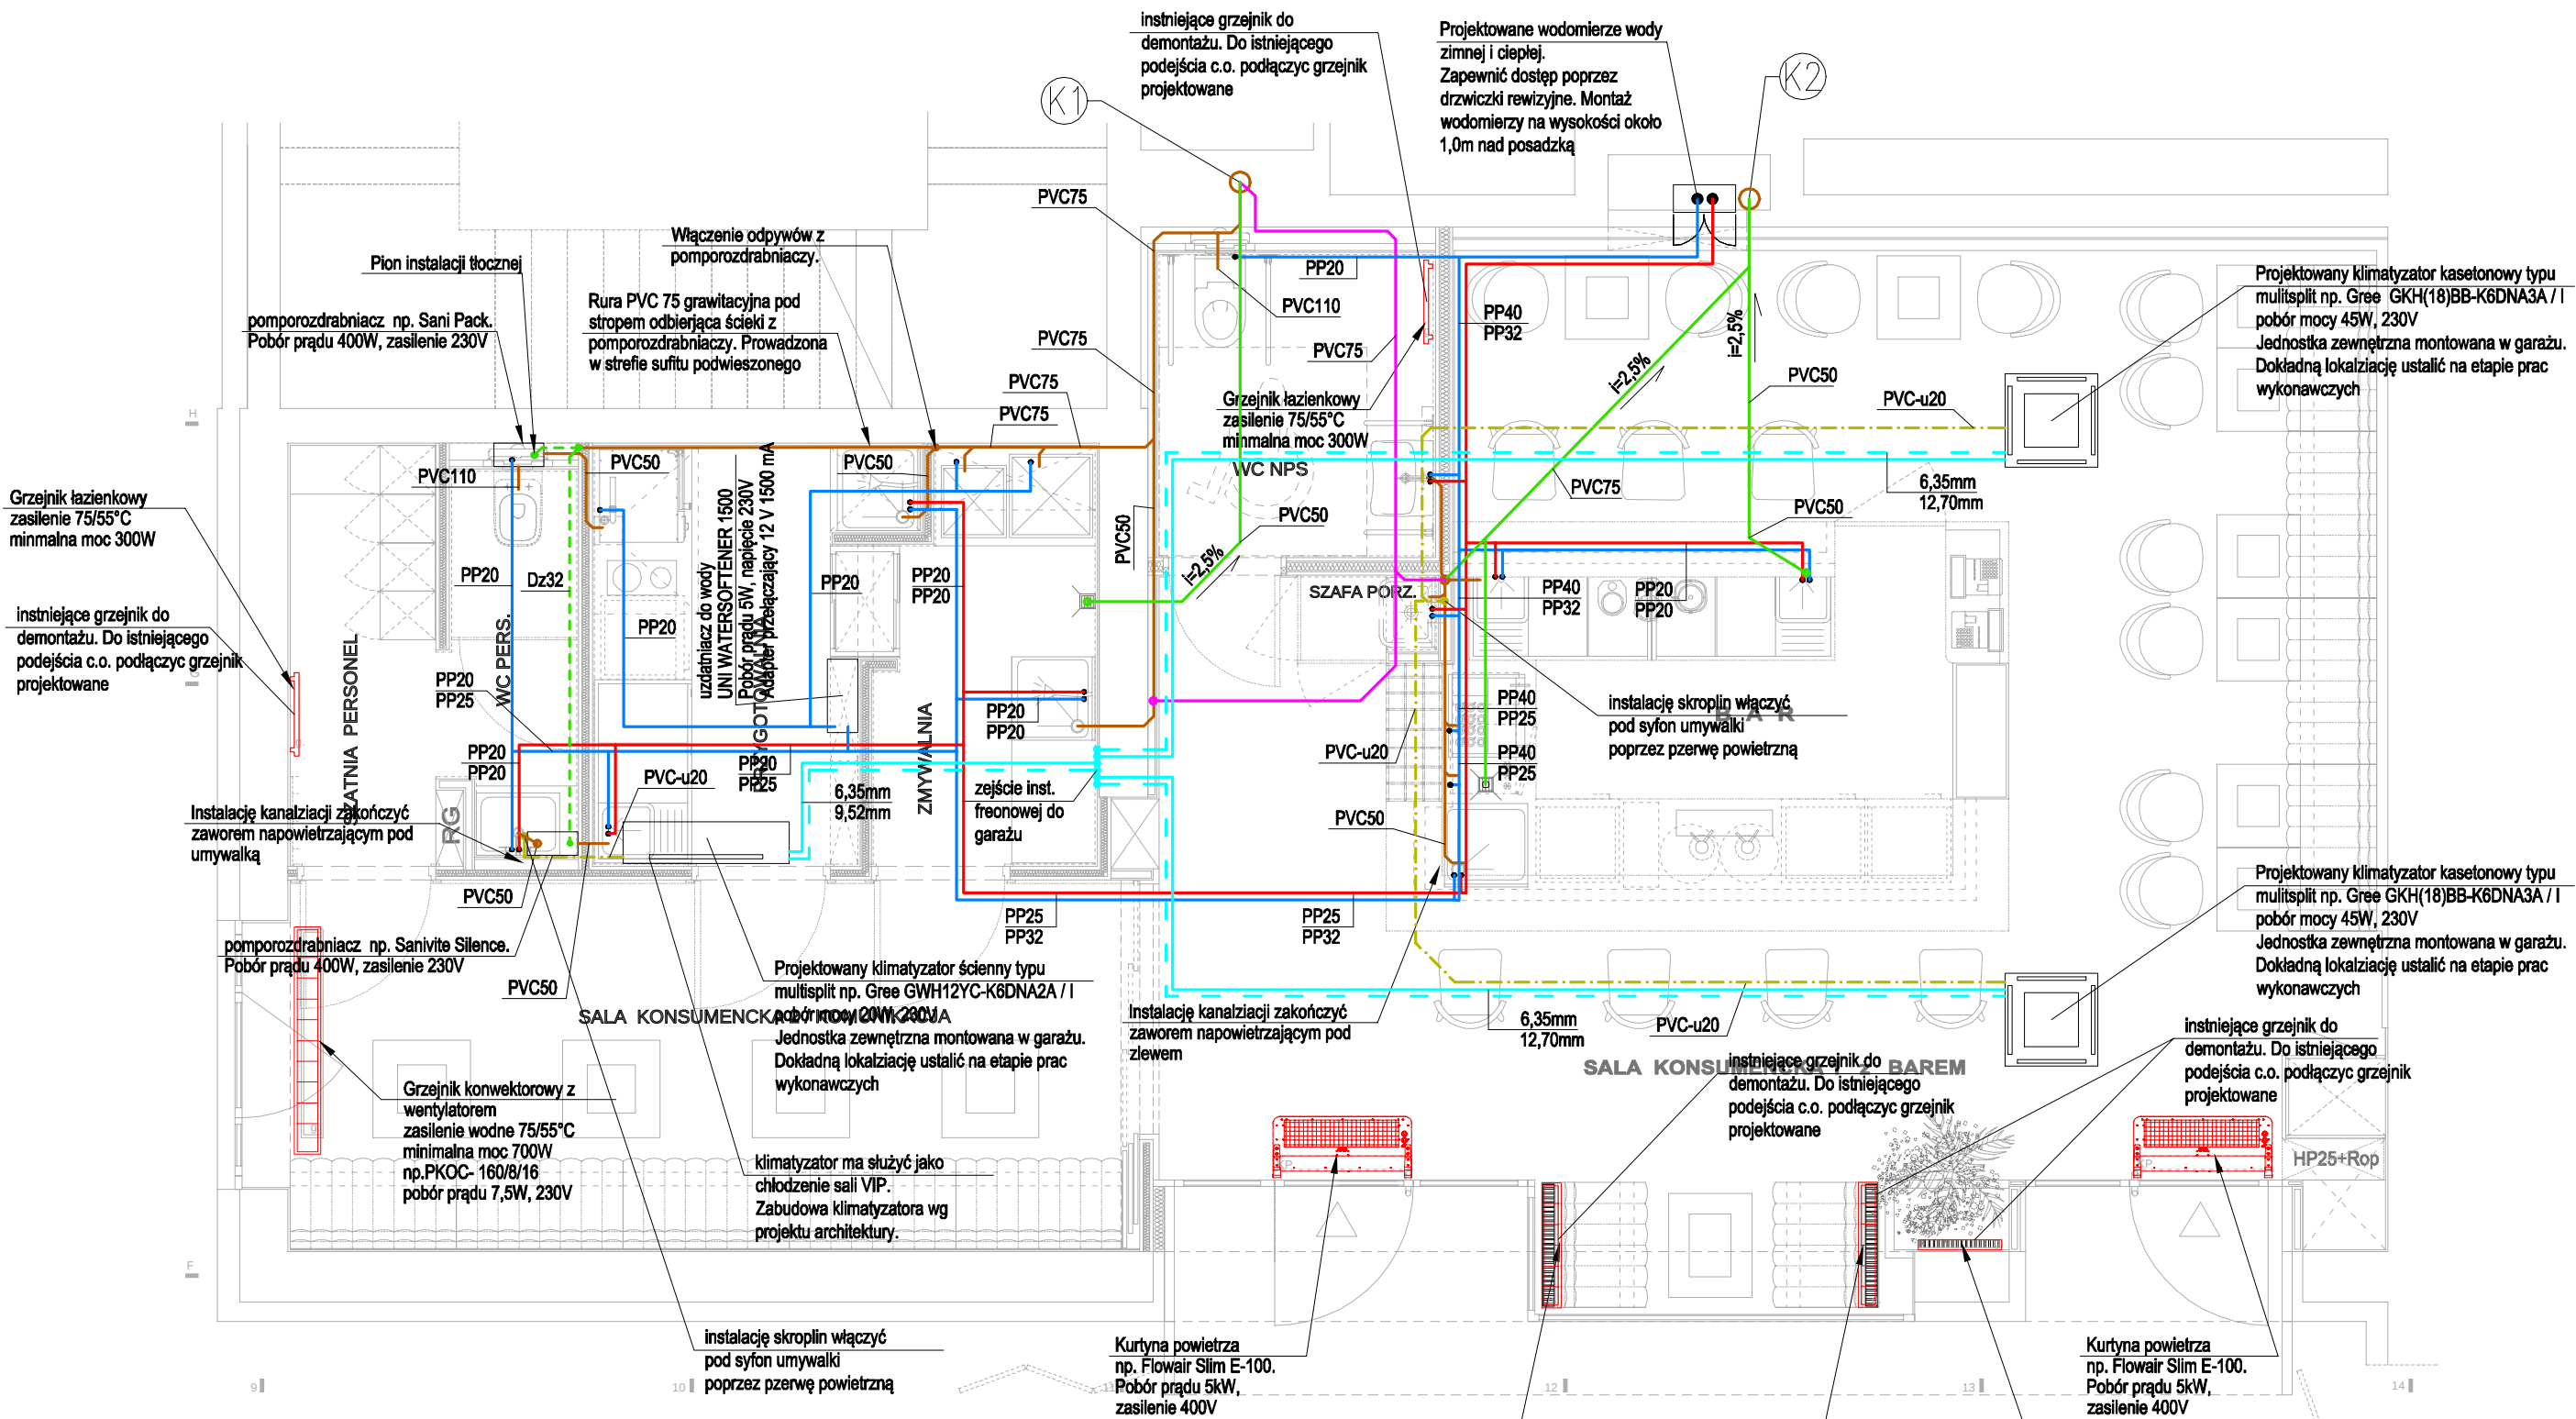

UWAGA

JEDNOSTKI WEWNĘTRZNE PODPIĄC DO
JEDNEJ JEDNOSTKI ZEWNĘTRZNEJ
TYPY MULTISPLIT.
NP. GREE GWH42JNK6LO
Pobór mocy 3,5kW, zasilanie 400V

OZNACZENIA:

- instalacja freonowa – gaz
- instalacja freonowa – ciecz
- instalacja skroplin
- instalacja zimnej wody
- instalacja ciepłej wody
- kanalizacja sanitarna prowadzone w przegrodzie pionowej lub po wierzchu ściany.
- kanalizacja sanitarna odpowietrzenie
- kanalizacja sanitarna prowadzona w warstwach posadzkowych
- kanalizacja sanitarna tłoczna w strefie sufitu podwieszonego



K1 istniejący pion kanalizacji sanitarnej

INWESTOR EXECUTIVE LOUNGE Sp. z o.o. UL. KROCHMALNA 59 LOK. U3 00-864 WARSZAWA GENERALNY PROJEKTANT / WYKONAWCA Toba Invest Sp. z o.o. ul.Erasmia Ciołka 17/202, 01-445 Warszawa www.tobainvest.pl, biuro@tobainvest.pl NAZWA PROJEKTU PROJEKT ADAPTACJI POW. USŁUGOWEJ NA CELE LOKALU GASTRONOMICZNEGO BAR & LOUNGE BROWARY WARSZAWSKIE		ADRES INWESTYCJI BUDYNEK BIUROWO-USŁUGOWY BROWARY WARSZAWSKIE UL. KROCHMALNA 59 / lok. U3 00-864 WARSZAWA GŁÓWNY PROJEKTANT mgr inż. Marcin Nowak MAZ/0349/PWOS/13 PROJEKTANCI mgr inż. Karolina Kotodziejczyk		BRANŻA SANITARNA PRZEZNACZENIE PROJEKT WYKONAWCZY TYTUŁ RYSUNKU INSTALACJA WOD-KAN I GRZEWCA DATA OPRACOWANIA 05.2021 SKALA / FORMAT 1:50 / A3 NR.RYS./REWIZJA PW.S.02_rew.555_06.21	
--	--	--	--	--	--



K1

NIENAJEŻE OPRACOWANIE STANOWI DZIEŁO AUTORSKIE I PODLEGA OCHRONIE ZAGRODZĄ Z USTAWĄ 83 Z DNIA 04.02.1984 O PRAWIE AUTORSKIM ORAZ PRAWACH POWIĄZANYCH. JEŚLI WYMAGANIE, ŻEBY WPROWADZENIE ZMIAN NA RYSUNKU TO MOŻE ONE BYĆ DOKONANE WYŁĄCZNIE PRZEZ AUTORA OPRACOWANIA PROJEKTOWEGO, PRZED PRZYSTĄPIENIEM DO PRAC WSZYSTKIE WYMIARY NALEŻY SPRAWDZIĆ W NATURZE NA BUDOWIE	
INWESTOR EXECUTIVE LOUNGE Sp. z o.o. UL. KROCHMALNA 59 LOK. U3 00-864 WARSZAWA	ADRES INWESTYCJI BUDYNEK BIUROWO-USŁUGOWY BROWARY WARSZAWSKIE UL. KROCHMALNA 59 / lok. U3 00-864 WARSZAWA
GENERALNY PROJEKTANT / WYKONAWCA TOBA Invest Sp. z o.o. ul.Erasmia Ciółka 17/202, 01-445 Warszawa www.tobainvest.pl, biuro@tobainvest.pl	GŁÓWNY PROJEKTANT mgr inż. Marcin Nowak MAZ/0349/PWOS/13
NAZWA PROJEKTU PROJEKT ADAPTACJI POW. USŁUGOWEJ NA CELE LOKALI GASTRONOMICZNEGO BAR & LOUNGE BROWARY WARSZAWSKIE	PROJEKTANCI mgr inż Karolina Kołodziejczyk
BRANŻA SANITARNA	
PRZEZNACZENIE PROJEKT WYKONAWCZY	
TYTUŁ RYSUNKU INSTALACJA KANALIZACJI ROZWINIĘCIE	
DATA OPRACOWANIA 05.2021	
SKALA / FORMAT 1:50 / A3	
NR.RYS./REWIZJA PW.S.04_rew.555_06.21	

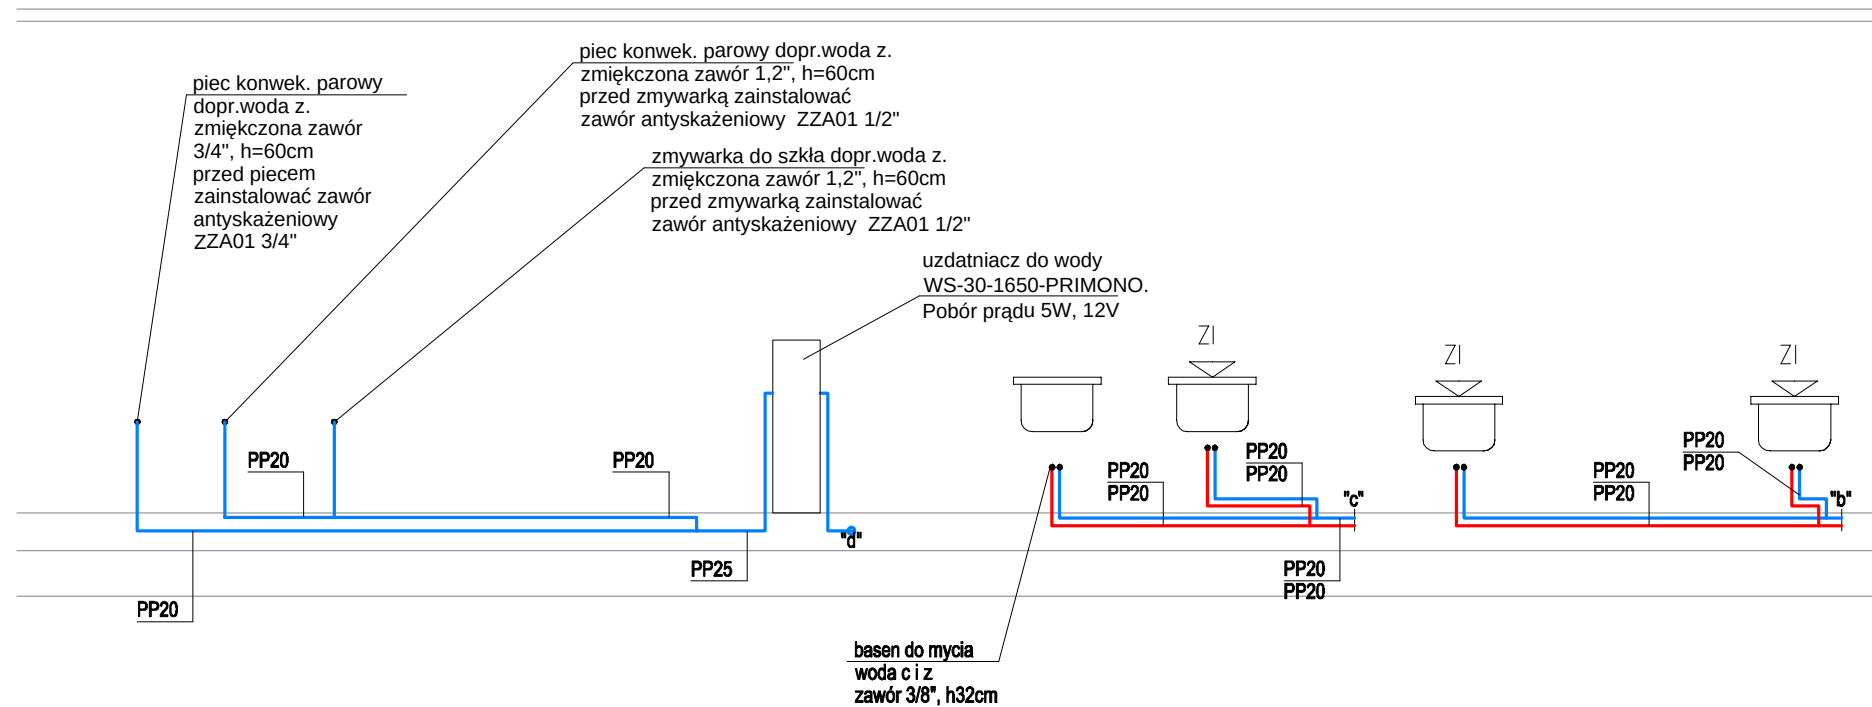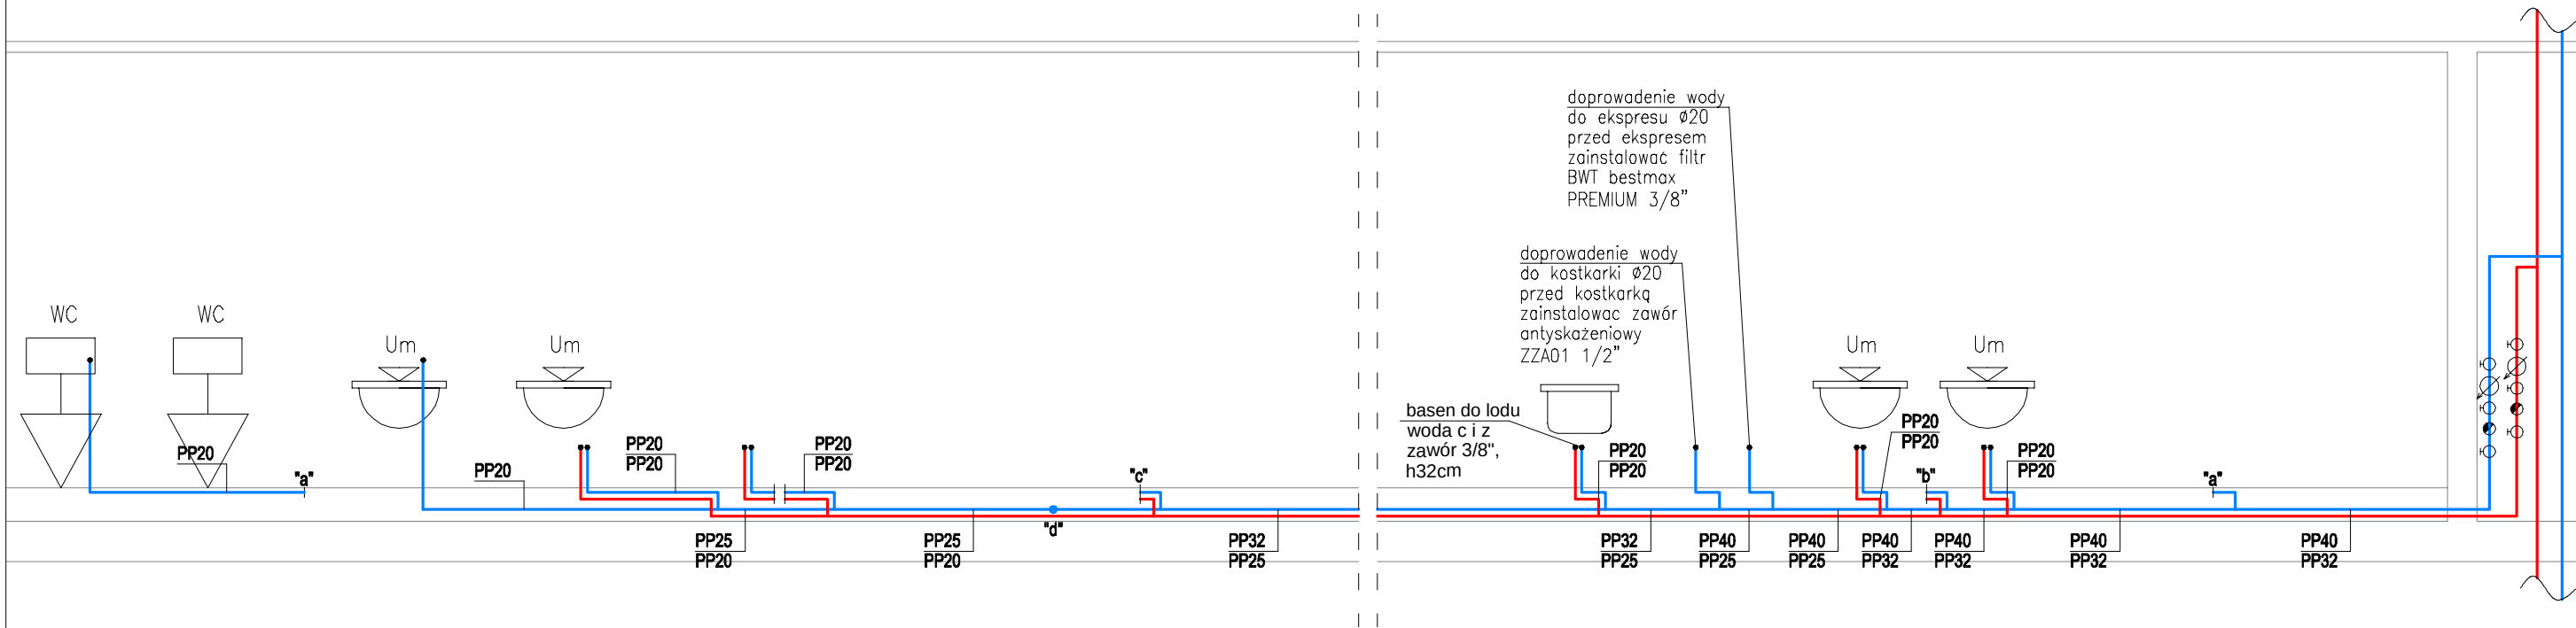

OZNACZENIA:

— instalacja zimnej wody

— instalacja ciepłej wody

Niniejsze opracowanie stanowi dzieło autorskie i podlega ochronie zgodnie z ustawą 83 z dnia 04.02.1994 o prawie autorskim oraz prawach pokrewnych. Jeśli wymagane jest wprowadzenie zmian na rysunku to mogą one być dokonane wyłącznie przez autora. Opracowania projektowego, przed przystąpieniem do prac wszystkie wymiary należy sprawdzić w naturze na budowie.	
INWESTOR EXECUTIVE LOUNGE Sp. z o.o. UL. KROCHMALNA 59 LOK. U3 00-864 WARSZAWA	ADRES INWESTYCJI BUDYNEK BIUROWO-USŁUGOWY BROWARY WARSZAWSKIE UL. KROCHMALNA 59 / lok. U3 00-864 WARSZAWA
GENERALNY PROJEKTANT / WYKONAWCA TOBA Invest Sp. z o.o. ul.Erazma Ciotka 17/202, 01-445 Warszawa www.tobainvest.pl, biuro@tobainvest.pl	GŁÓWNY PROJEKTANT mgr inż. Marcin Nowak MAZ/0349/PWOS/13
NAZWA PROJEKTU PROJEKT ADAPTACJI POW. USŁUGOWEJ NA CELE LOKALU GASTRONOMICZNEGO BAR & LOUNGE BROWARY WARSZAWSKIE	PROJEKTANCI mgr inż. Karolina Kołodziejczyk
BRANZA SANITARNA	
PRZEZNACZENIE PROJEKT WYKONAWCZY	
TYTUŁ RYSUNKU INSTALACJA WODY ROZWINIĘCIE	
DATA OPRACOWANIA 05.2021	
SKALA / FORMAT 1:50 / A3	
NR.RYS./REWIZJA PW.S.05_rew.555_06.21	